

CONSERVATION DU CADASTRE

COPROPRIETE

Esquisse d'étages

Document établi en application de la loi du 31 mars 1884
applicable dans les départements de la Moselle, du Bas-Rhin et du Haut-Rhin

Documents établis à partir du levé effectué le 09/01/2026

Situation	Commune : GAMBSHEIM
	Section : 3
	N° du plan : 206
	Rue, n° : 39, route Nationale

Esquisse établie et certifiée exacte
par le cabinet **GRAFF-KIEHL, Géomètres Experts Associés**
à Strasbourg, le 21 janvier 2026



Plan de situation



ETAT DESCRIPTIF DE DIVISION

N° de la P.C.	Propriétaires	Situation, nature et description du local
PC1	L'ensemble des propriétaires de l'immeuble sis 39, route Nationale à GAMBSHEIM, en indivision pour un total de 10000/10000èmes (lots 1 à 11). Tantièmes calculés conformément aux dispositions de l'article 5 de la loi du 10 juillet 1965.	Les parties communes générales à savoir : le sol bâti et non bâti cadastré à GAMBSHEIM, section 03, parcelle 206, d'une surface cadastrale de 5a 31ca. Les charges générales (contributions foncières, taxes, primes d'assurances, etc..). <u>A l'extérieur :</u> Une aire de circulation et une aire de présentation des poubelles.
PC2	Les propriétaires des lots 1 à 5 en indivision forcée pour un total de 10000/10000èmes.	Les fondations, l'ossature, les murs et la toiture du bâtiment A. Les éléments d'équipement communs y compris les parties de canalisations y afférentes traversant des locaux privés. <u>Au sous-sol :</u> Un dégagement. <u>Du sous-sol au rez-de-chaussée :</u> Un escalier. <u>Au rez-de-chaussée :</u> Un dégagement et trois locaux communs.

NOTA BENE :

- Tantièmes calculés conformément aux instructions de juin 1998 du Conseil Supérieur de l'Ordre des Géomètres Experts.
- Tout changement dans la consistance d'un ou plusieurs lots devra faire l'objet d'une modification dans la répartition des tantièmes de copropriété.
- Tout lot de copropriété dont la surface est inférieure à 14m² (h>1.80m) ou dont le volume est inférieur à 33m³ ne peut être destiné à l'habitation.

<u>Coefficients de pondération utilisés :</u>		
- Appartement (> 1,80m)		1
- Appartement (< 1,80m)		0,4
- Parking couvert		0,3
- Balcon		0,2
- Grange		0,2
- Cave		0,2
- Abri		0,2
- Parking plein air		0,15
- Jardin privatif		0,05

ETAT DESCRIPTIF DE DIVISION



N° du lot	Propriétaires	Situation, nature et description du local	N° de voirie	Bât.	Esc.	Niv.	Loc.	Surface (en m²)	QP dans la copropriété du sol PC1	QP PC2	QP PC3	QP PC4	QP PC5	QP PC6	QP PC7	QP PC8	QP PC9	QP PC10	QP PC11	QP PC12	QP PC13	QP PC14	QP PC15	QP PC16
1		<i>Dans le bâtiment A, un appartement duplex comprenant :</i> <u>Au sous-sol :</u> La cave n°3 et un dégagement. <u>Du sous-sol au rez-de-chaussée :</u> Un escalier. <u>Au rez-de-chaussée :</u> Une entrée/cuisine, un salon/séjour, une salle de bains et un W.C. <u>Du rez-de-chaussée à l'étage :</u> Un escalier. <u>A l'étage :</u> Un dégagement et deux chambres. Appartement (> 1,80m) Cave	39	A		0	1	60,8 21,5	3109	3579														
2		<i>Dans le bâtiment A, un appartement comprenant :</i> <u>Au rez-de-chaussée :</u> Un dégagement, un salon/séjour, une salle de bains, un W.C et deux chambres. Appartement (> 1,80m)	39	A		0	2	49,3	2354	2711														
3		<i>Dans le bâtiment A, un appartement comprenant :</i> <u>Du rez-de-chaussée à l'étage :</u> Un escalier. <u>A l'étage :</u> Un dégagement, un salon/séjour, une salle de bains, un W.C, trois chambres et un balcon. Appartement (> 1,80m) Appartement (< 1,80m) Balcon	39	A		1	1	56,5 12,4 1,8	2954	3400														
4		<u>Au sous-sol du bâtiment A :</u> La cave n°1. Cave	39	A		81	1	9,8	93	107														
5		<u>Au sous-sol du bâtiment A :</u> La cave n°2. Cave	39	A		81	2	18,5	177	203														

ETAT DESCRIPTIF DE DIVISION

N° du lot	Propriétaires	Situation, nature et description du local	N° de voirie	Bât.	Esc.	Niv.	Loc.	Surface (en m²)	QP dans la copropriété du sol PC1	QP PC2	QP PC3	QP PC4	QP PC5	QP PC6	QP PC7	QP PC8	QP PC9	QP PC10	QP PC11	QP PC12	QP PC13	QP PC14	QP PC15	QP PC16
6		Les fondations, l'ossature, les murs et la toiture du bâtiment B. <u>A l'extérieur :</u> Le jardin n°1 et le parking couvert n°6. <u>Au rez-de-chaussée :</u> Une grange. Grange Parking couvert Jardin privatif	39	B		0	1	51,2 22,8 22,5	868															
7		<u>A l'extérieur :</u> Le parking n°1. Parking plein air					1	12,5	89															
8		<u>A l'extérieur :</u> Le parking n°2. Parking plein air					2	12,5	89															
9		<u>A l'extérieur :</u> Le parking n°3. Parking plein air					3	12,5	89															
10		<u>A l'extérieur :</u> Le parking n°4. Parking plein air					4	12,5	89															
11		<u>A l'extérieur :</u> Le parking n°5. Parking plein air					5	12,5	89															
TOTAUX :									10000	10000														

25602

PLAN DE MASSE

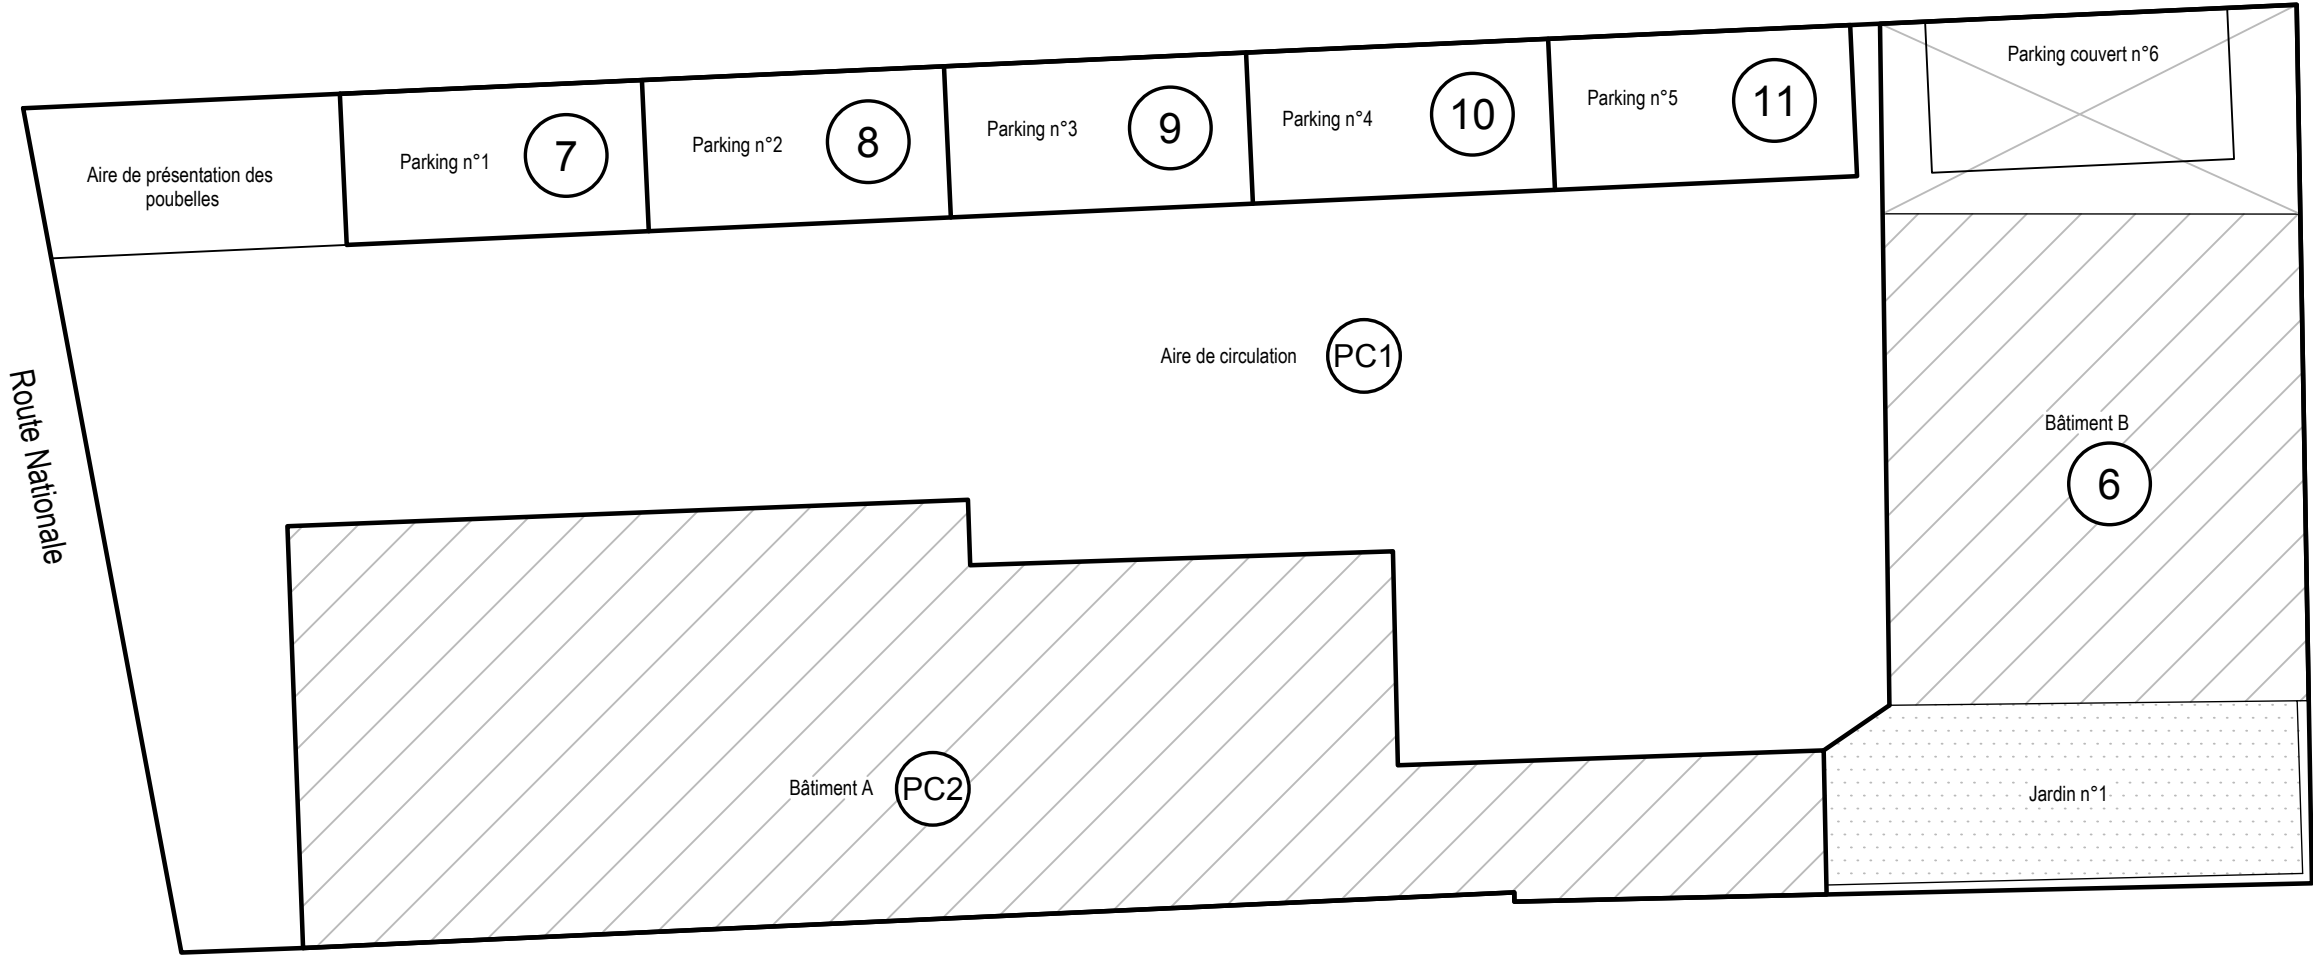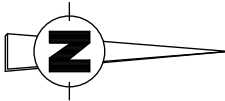

GRAFF - KIEHL Géomètres Experts

4 bld de la Dordogne STRASBOURG
BP 60001 - 67001 STRASBOURG CEDEX
1a rue du Ried SCHWEIGHOUSE SUR MODER
BP 90353 - 67507 HAGUENAU CEDEX
Tél. 03 88 36 77 02 - Fax : 03 88 36 90 97
cabinet@graff-kiehl.fr - www.graff-kiehl.fr




Echelle : 1/125 (impression A3)

25602

SOUS-SOL

Bâtiment A

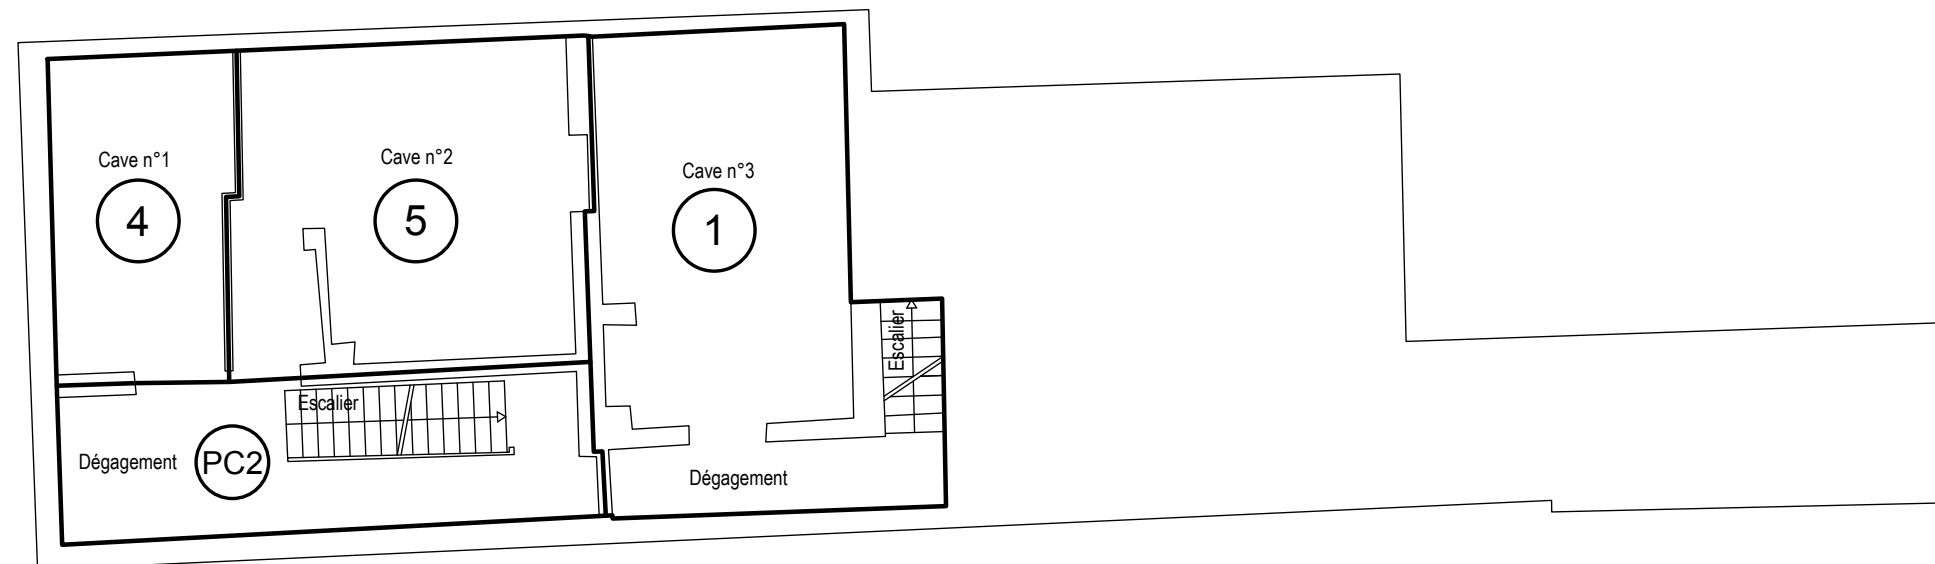

GRAFF - KIEHL Géomètres Experts

4 bld de la Dordogne STRASBOURG
BP 60001 - 67001 STRASBOURG CEDEX

1a rue du Ried SCHWEIGHOUSE SUR MODER
BP 90353 - 67507 HAGUENAU CEDEX

Tél. 03 88 36 77 02 - Fax : 03 88 36 90 97
cabinet@graff-kiehl.fr - www.graff-kiehl.fr

1.0m




5.0m

Echelle : 1/100 (impression A3)


25602

REZ-DE-CHAUSSEE

Bâtiment B

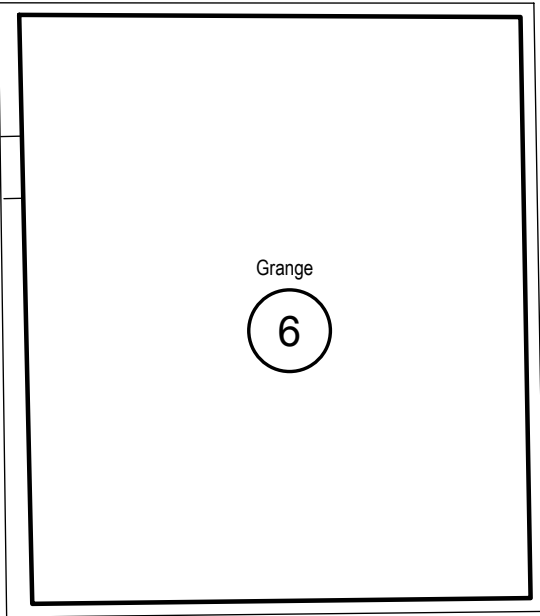

Bâtiment A

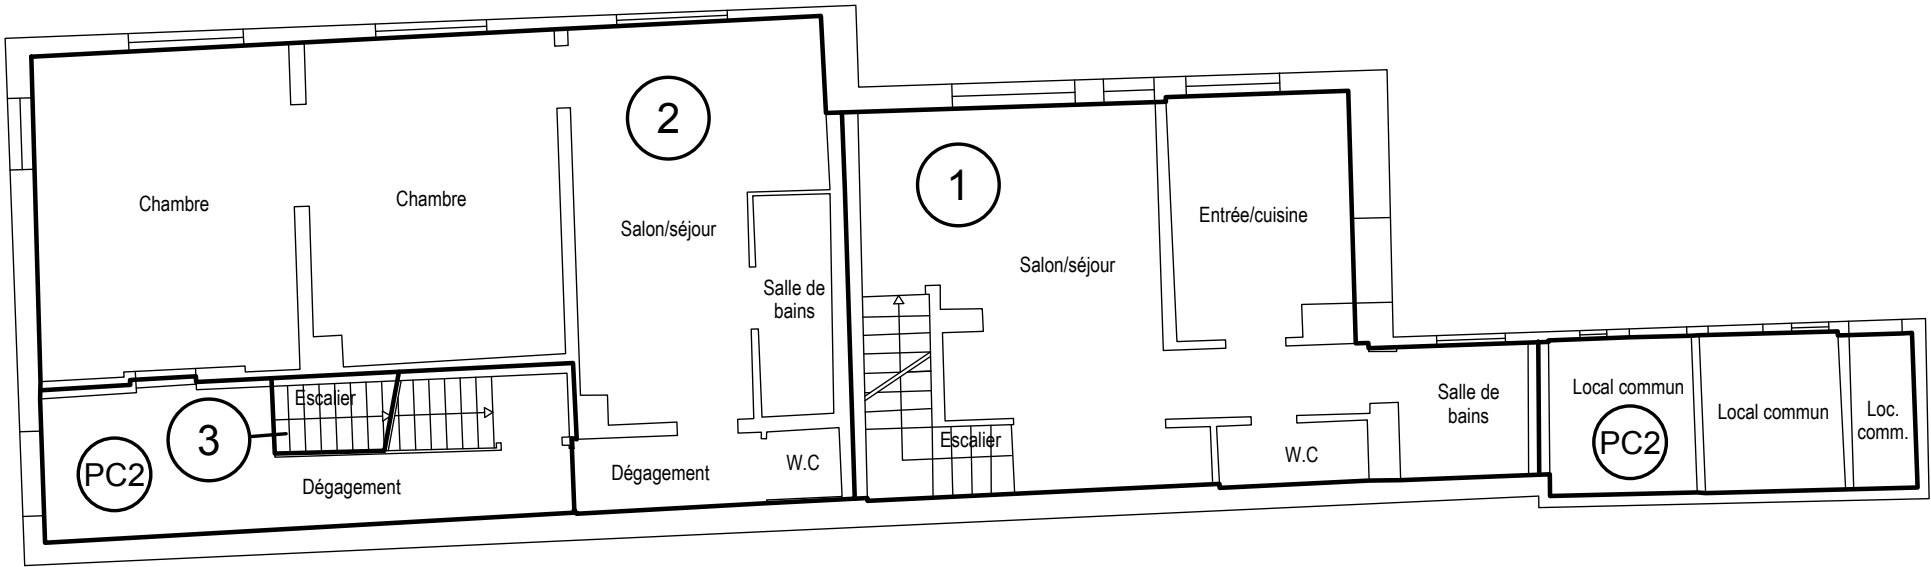

GRAFF - KIEHL Géomètres Experts

4 bld de la Dordogne STRASBOURG
BP 60001 - 67001 STRASBOURG CEDEX
1a rue du Ried SCHWEIGHOUSE SUR MODER
BP 90353 - 67507 HAGUENAU CEDEX
Tél. 03 88 36 77 02 - Fax : 03 88 36 90 97
cabinet@graff-kiehl.fr - www.graff-kiehl.fr




Echelle : 1/100 (impression A3)

25602

ETAGE

Bâtiment A

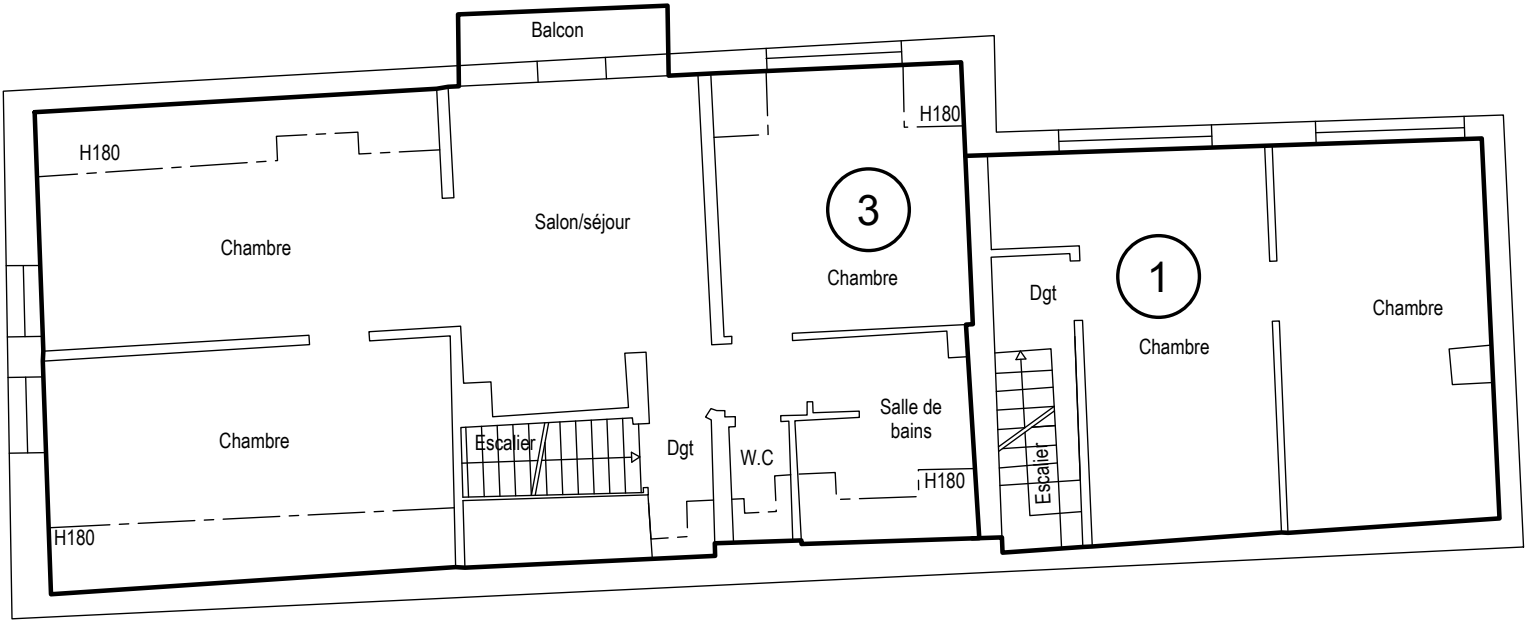

GRAFF - KIEHL Géomètres Experts

4 bld de la Dordogne STRASBOURG
BP 60001 - 67001 STRASBOURG CEDEX
1a rue du Ried SCHWEIGHOUSE SUR MODER
BP 90353 - 67507 HAGUENAU CEDEX
Tél. 03 88 36 77 02 - Fax : 03 88 36 90 97
cabinet@graff-kiehl.fr - www.graff-kiehl.fr

1.0m 5.0m

Echelle : 1/100 (impression A3)